INTERIOR DESIGN DRAWING FOR

FOR

THE CROWNED ELEGANCE HOME

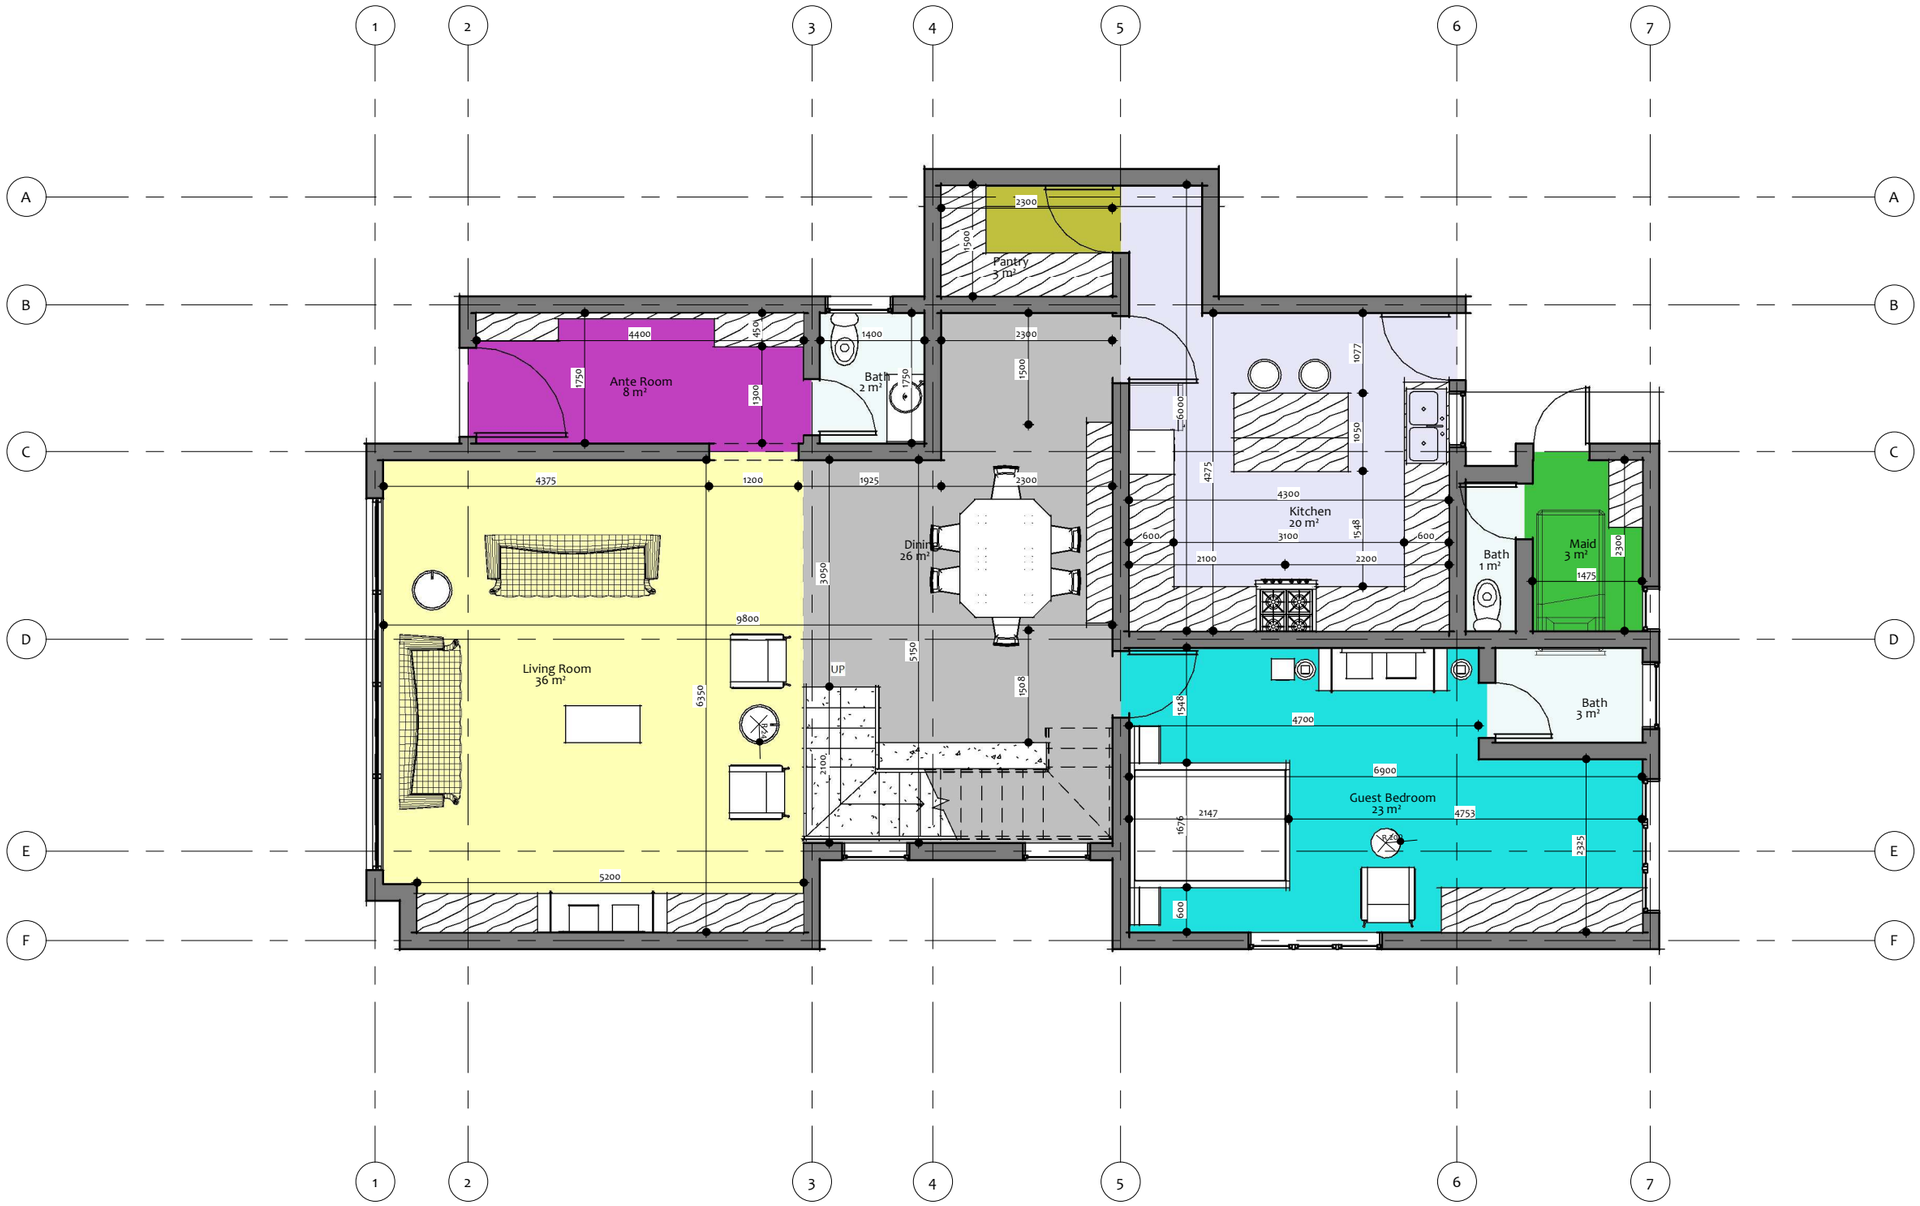

01 GF FURNITURE PLAN & LAYOUT

1 : 75

APPROVAL COLUMN:

ARC. SEAL

SN	NOTES
1	Do not scale this drawing. Work with the provided dimemnsion.
2	Note that all dimensions are in millimeter (mm).
3	The Architect is not liable for any defect on the buildings of which the construction he does not supervise

INTERIOR DESIGNER

SHAN INTERIOR

PROJECT:

INTERIOR DESIGN, FIT-OUT AND IMPLEMENTATION OF A 4-BEDROOM MONOPLEX RESIDENTIAL BUILDING

SHEET NAME	GF FURNITURE PLAN	
	Sheet No.	A101
	Scale	

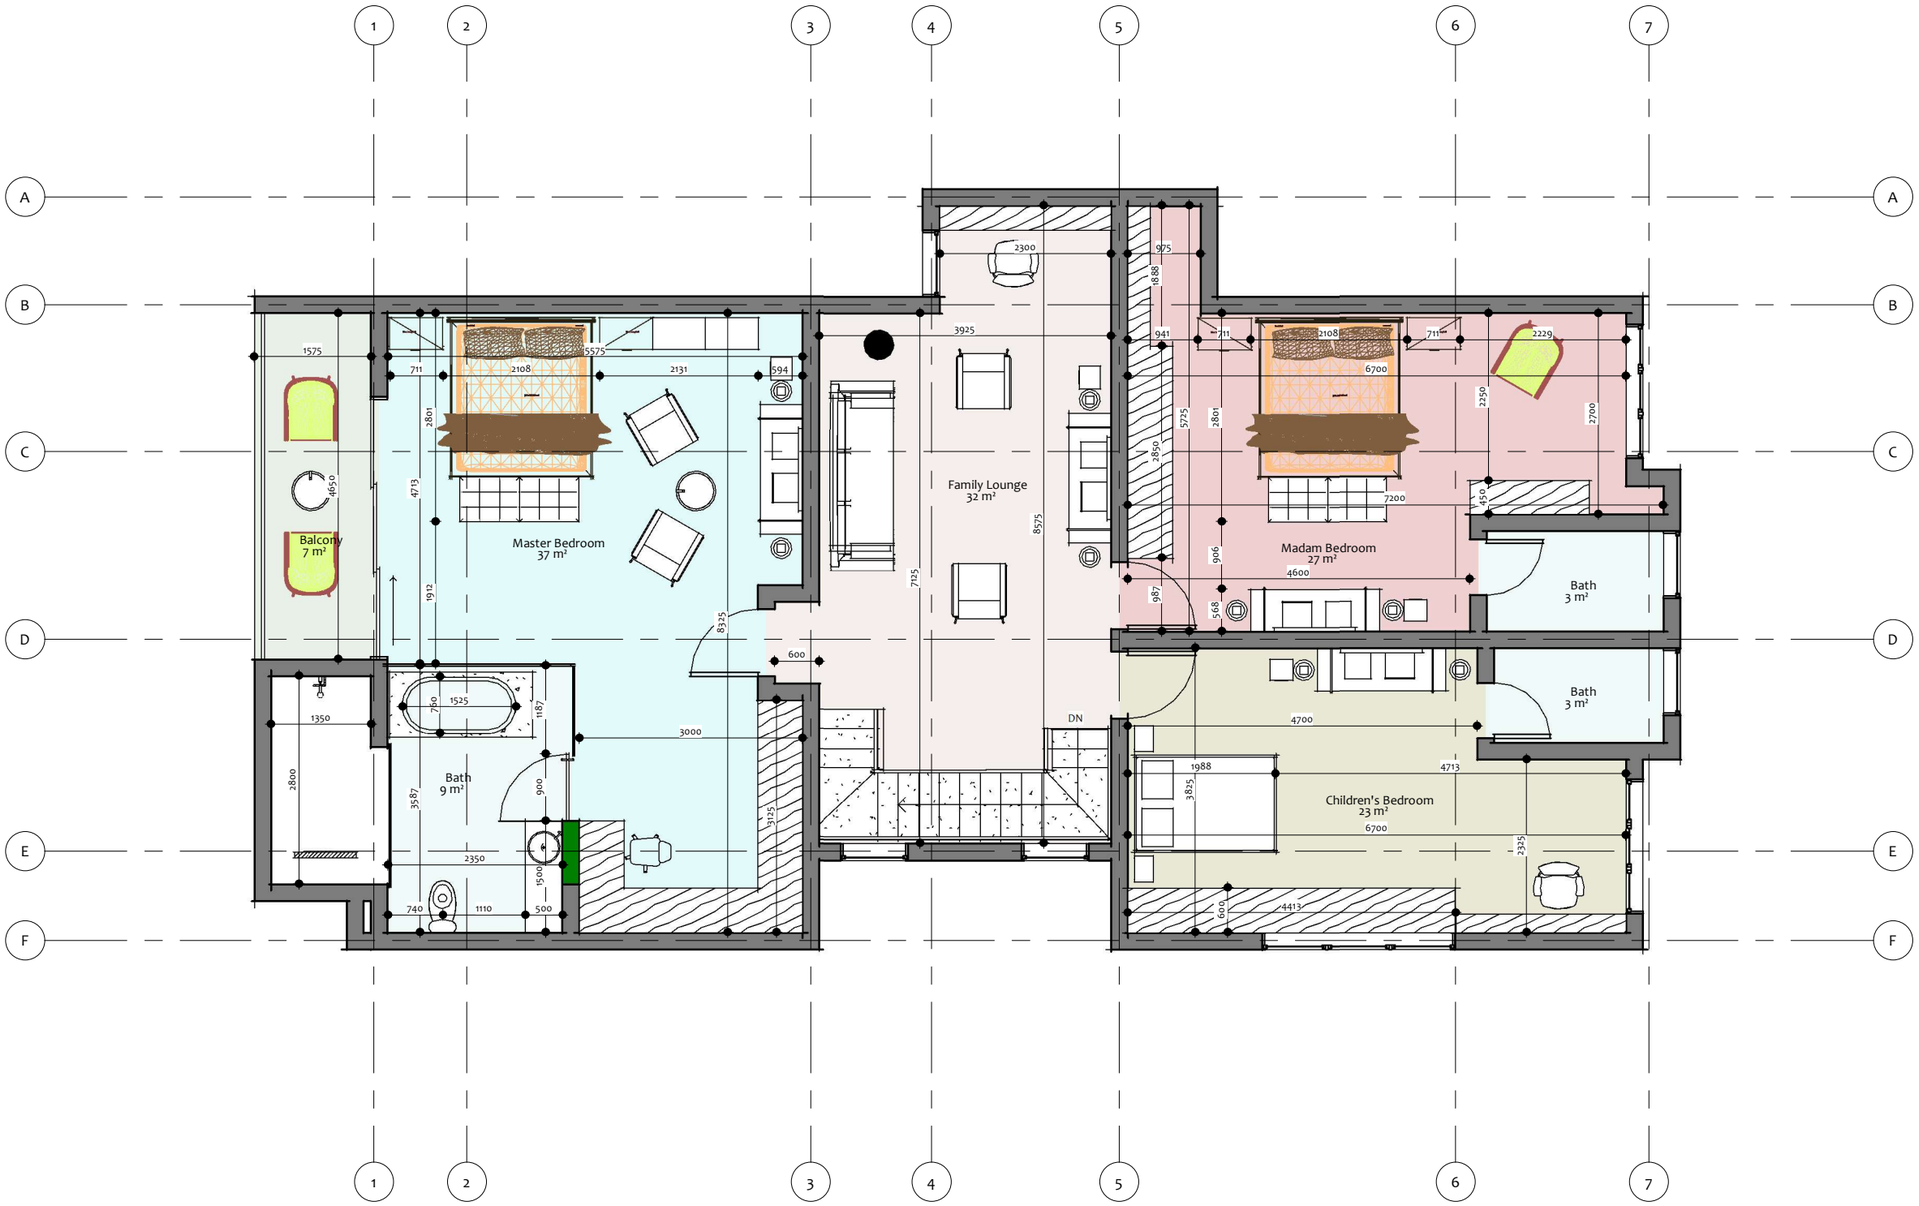

02 FF FURNITURE PLA & LAYOUT

1

1 : 75

APPROVAL COLUMN:

ARC. SEAL

SN	NOTES
1	Do not scale this drawing. Work with the provided dimemnsion.
2	Note that all dimensions are in millimeter (mm).
3	The Architect is not liable for any defect on the buildings of which the construction he does not supervise

INTERIOR DESIGNER

SHAN INTERIOR

PROJECT:

INTERIOR DESIGN, FIT-OUT AND IMPLEMENTATION OF A 4-BEDROOM MONOPLEX RESIDENTIAL BUILDING

SHEET NAME	FF FURNITURE PLAN	
	Sheet No.	A102
	Scale	

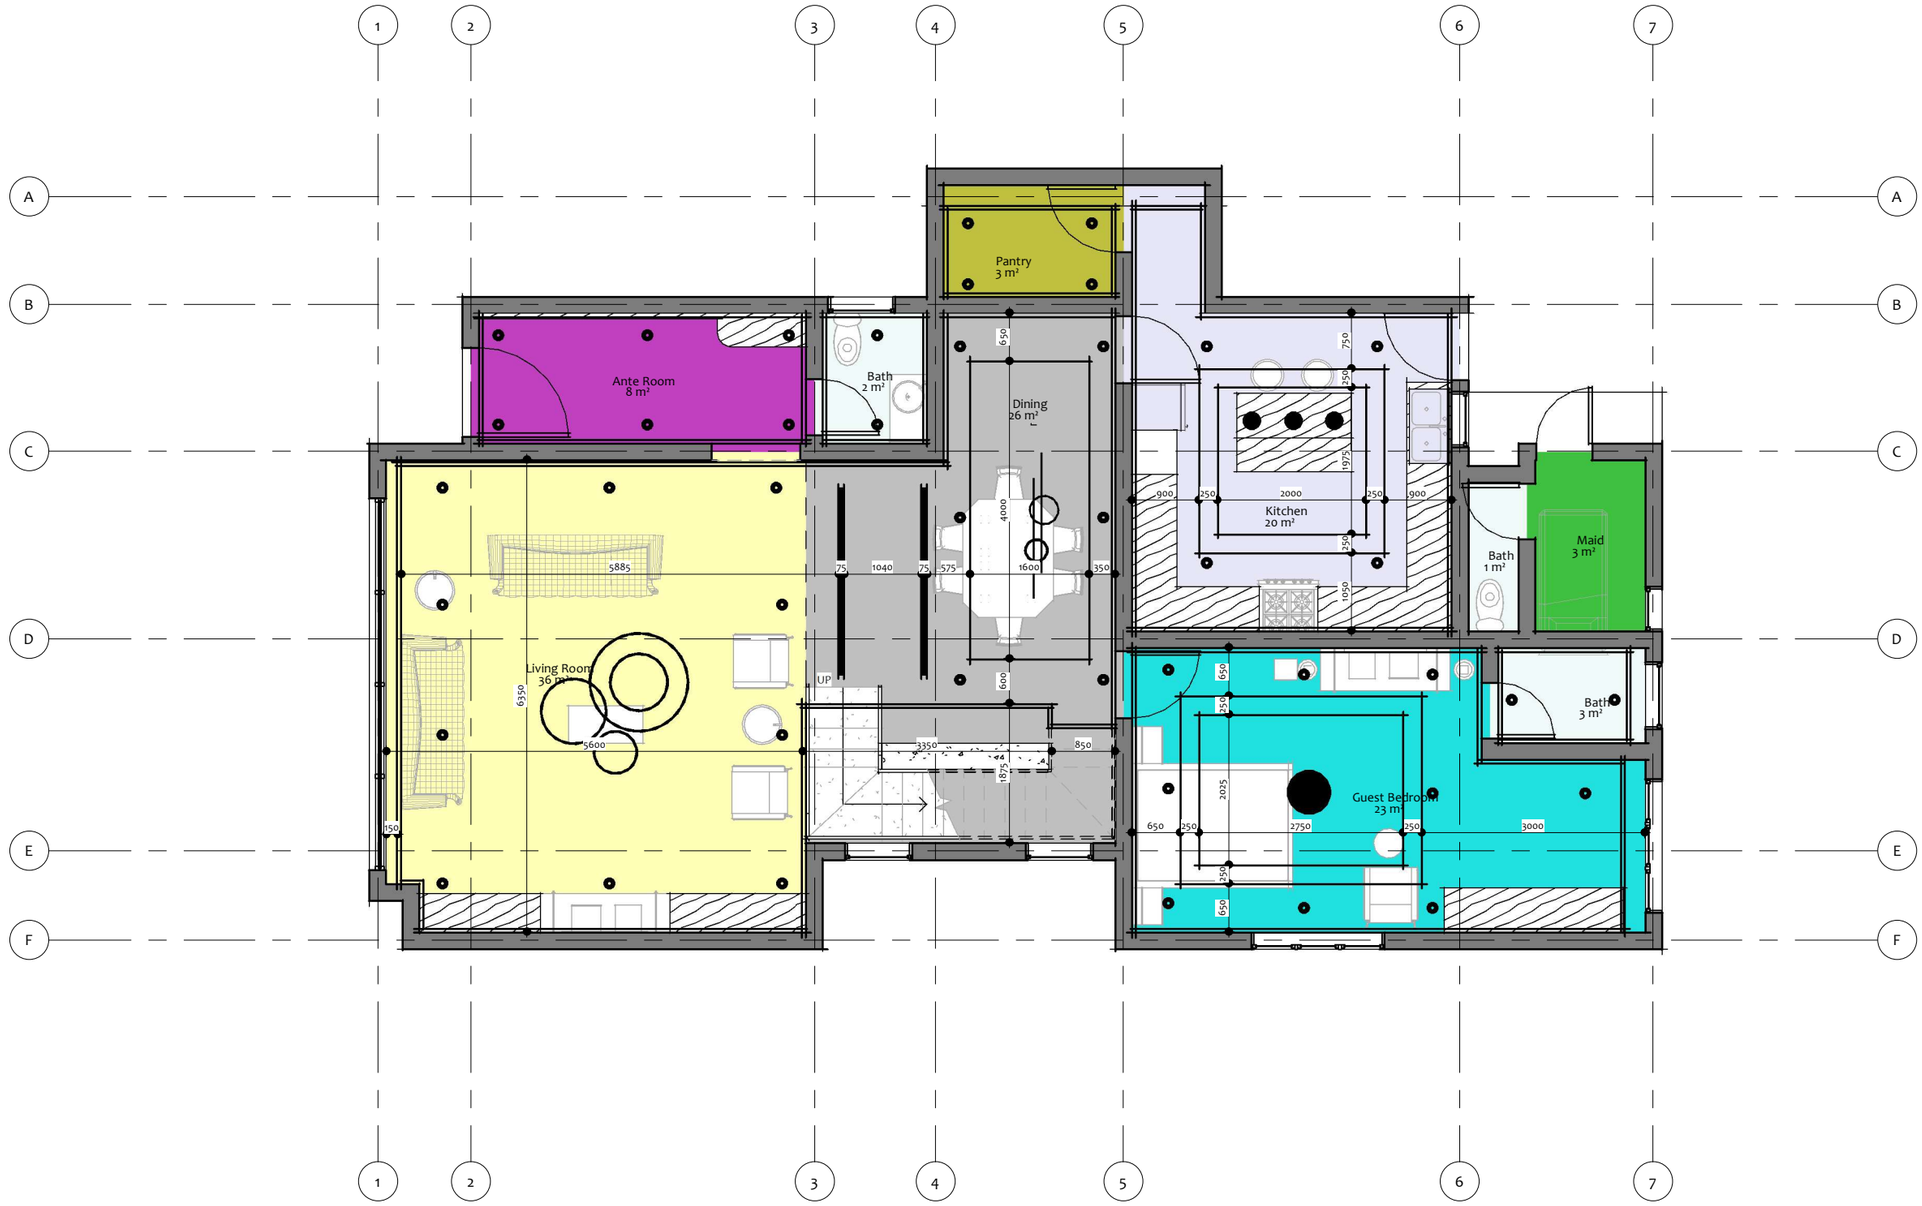

1

03 GF CEILING & LIGHTING PLAN

1 : 75

APPROVAL COLUMN:

ARC. SEAL

SN	NOTES
1	Do not scale this drawing. Work with the provided dimemnsion.
2	Note that all dimensions are in millimeter (mm).
3	The Architect is not liable for any defect on the buildings of which the construction he does not supervise

INTERIOR DESIGNER

SHAN INTERIOR

PROJECT:

INTERIOR DESIGN, FIT-OUT AND IMPLEMENTATION OF A 4-BEDROOM MONOPLEX RESIDENTIAL BUILDING

SHEET NAME	GF CEILING AND LIGHTING PLAN	
	Sheet No.	A103
	Scale	

04 FF CEILING AND LIGHTING PLAN

1

1 : 75

APPROVAL COLUMN:

ARC. SEAL

SN	NOTES
1	Do not scale this drawing. Work with the provided dimemnsion.
2	Note that all dimensions are in millimeter (mm).
3	The Architect is not liable for any defect on the buildings of which the construction he does not supervise

INTERIOR DESIGNER

SHAN INTERIOR

PROJECT:

INTERIOR DESIGN, FIT-OUT AND IMPLEMENTATION OF A 4-BEDROOM MONOPLEX RESIDENTIAL BUILDING

SHEET NAME	FF CEILING AND FURNITURE PLAN	
	Sheet No.	A104
	Scale	

05 GF AC LAYOUT

1 : 75

APPROVAL COLUMN:

ARC. SEAL

SN	NOTES
1	Do not scale this drawing. Work with the provided dimemnsion.
2	Note that all dimensions are in millimeter (mm).
3	The Architect is not liable for any defect on the buildings of which the construction he does not supervise

INTERIOR DESIGNER

SHAN INTERIOR

PROJECT:

INTERIOR DESIGN, FIT-OUT AND IMPLEMENTATION OF A 4-BEDROOM MONOPLEX RESIDENTIAL BUILDING

SHEET NAME	GF AC LAYOUT	
	Sheet No.	A105
	Scale	

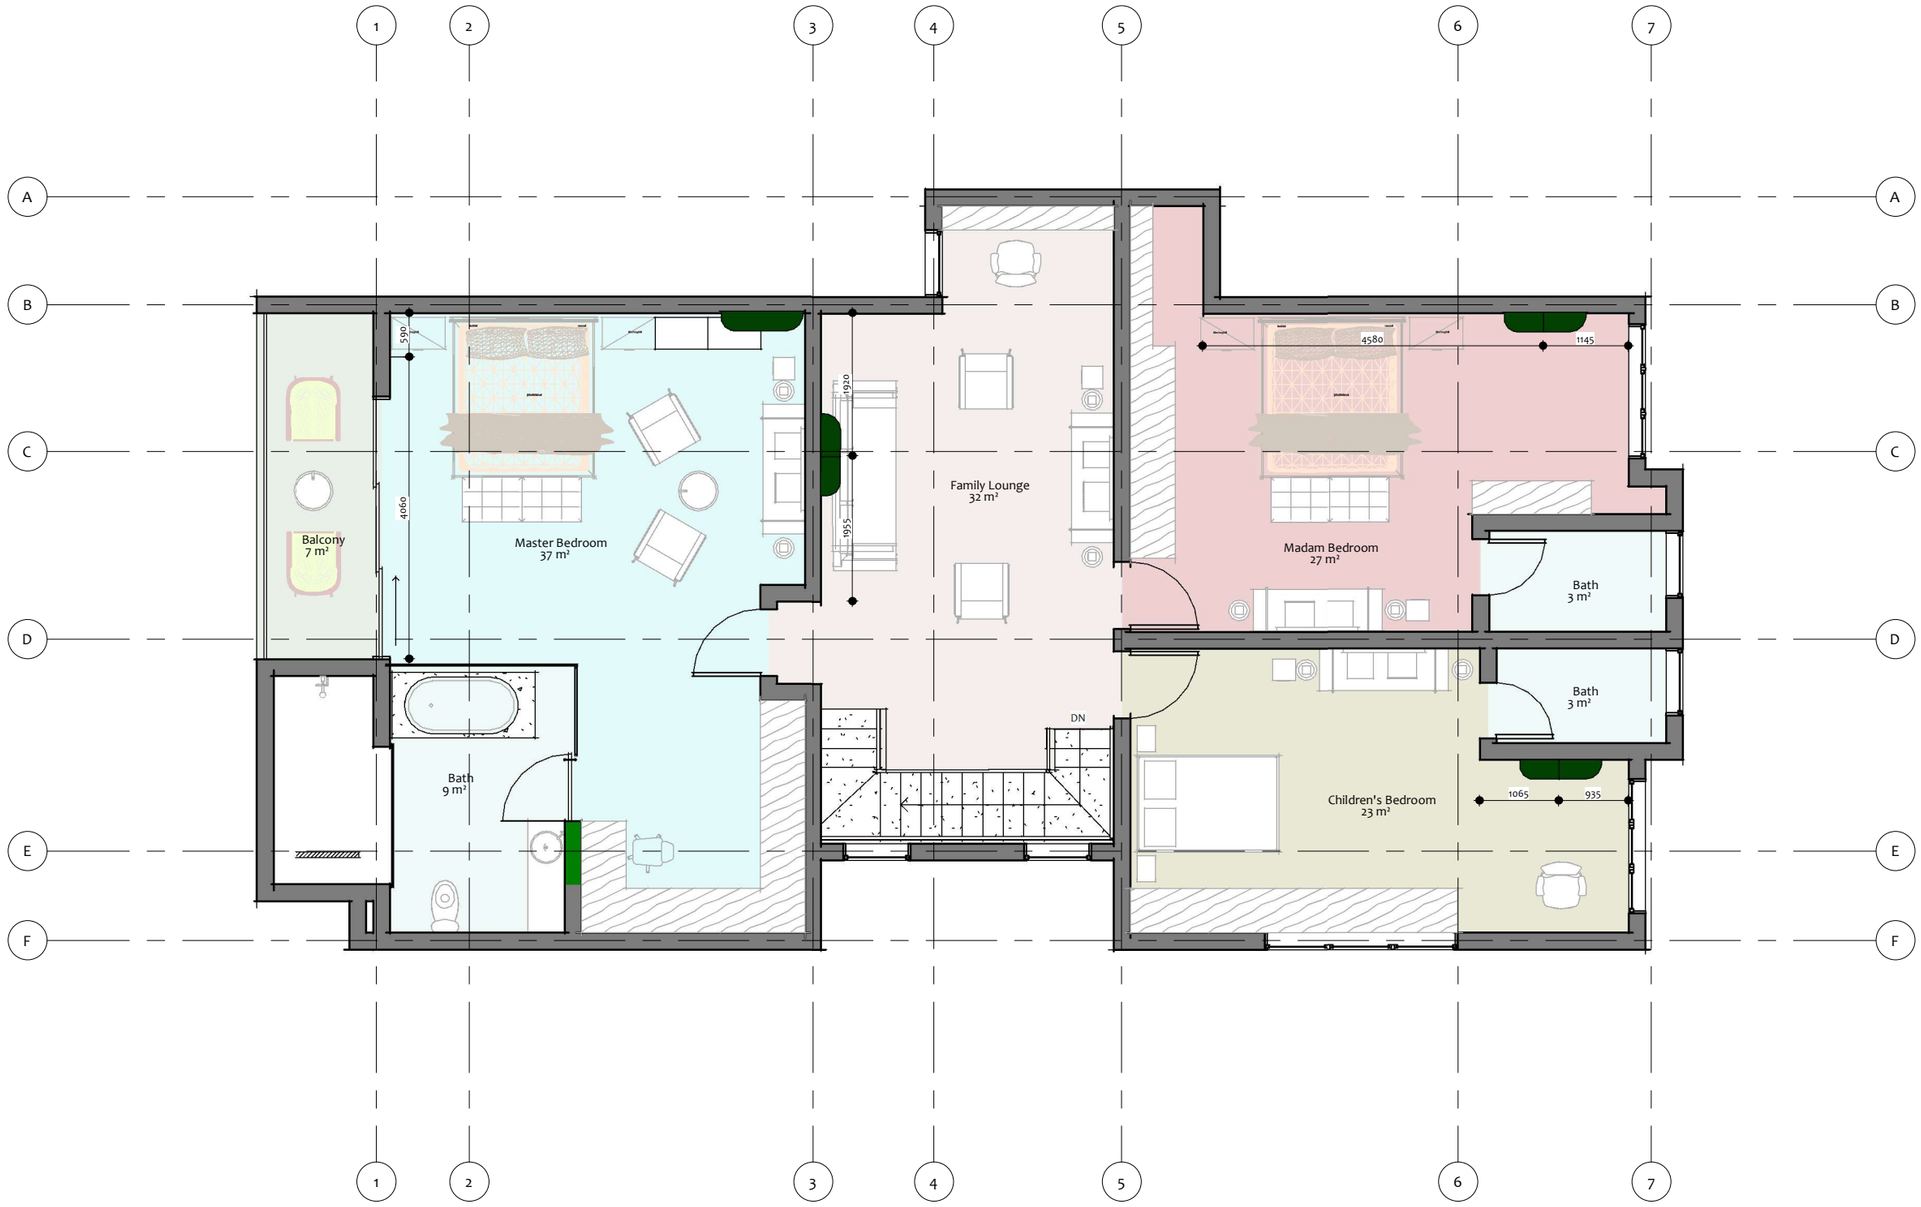

06 FF AC LAYOUT

1

1 : 75

APPROVAL COLUMN:

ARC. SEAL

SN	NOTES
1	Do not scale this drawing. Work with the provided dimemnsion.
2	Note that all dimensions are in millimeter (mm).
3	The Architect is not liable for any defect on the buildings of which the construction he does not supervise

INTERIOR DESIGNER

SHAN INTERIOR

PROJECT:

INTERIOR DESIGN, FIT-OUT AND IMPLEMENTATION OF A 4-BEDROOM MONOPLEX RESIDENTIAL BUILDING

SHEET NAME	FF AC LAYOUT	
	Sheet No.	A106
	Scale	